RIVERSIDE DISTRICT

TECHNICAL DRAWING SET / CONCEPT DESIGN / REVISION B

XT SOLUTION

SAMPLE DOCUMENT - NOT FOR CONSTRUCTION

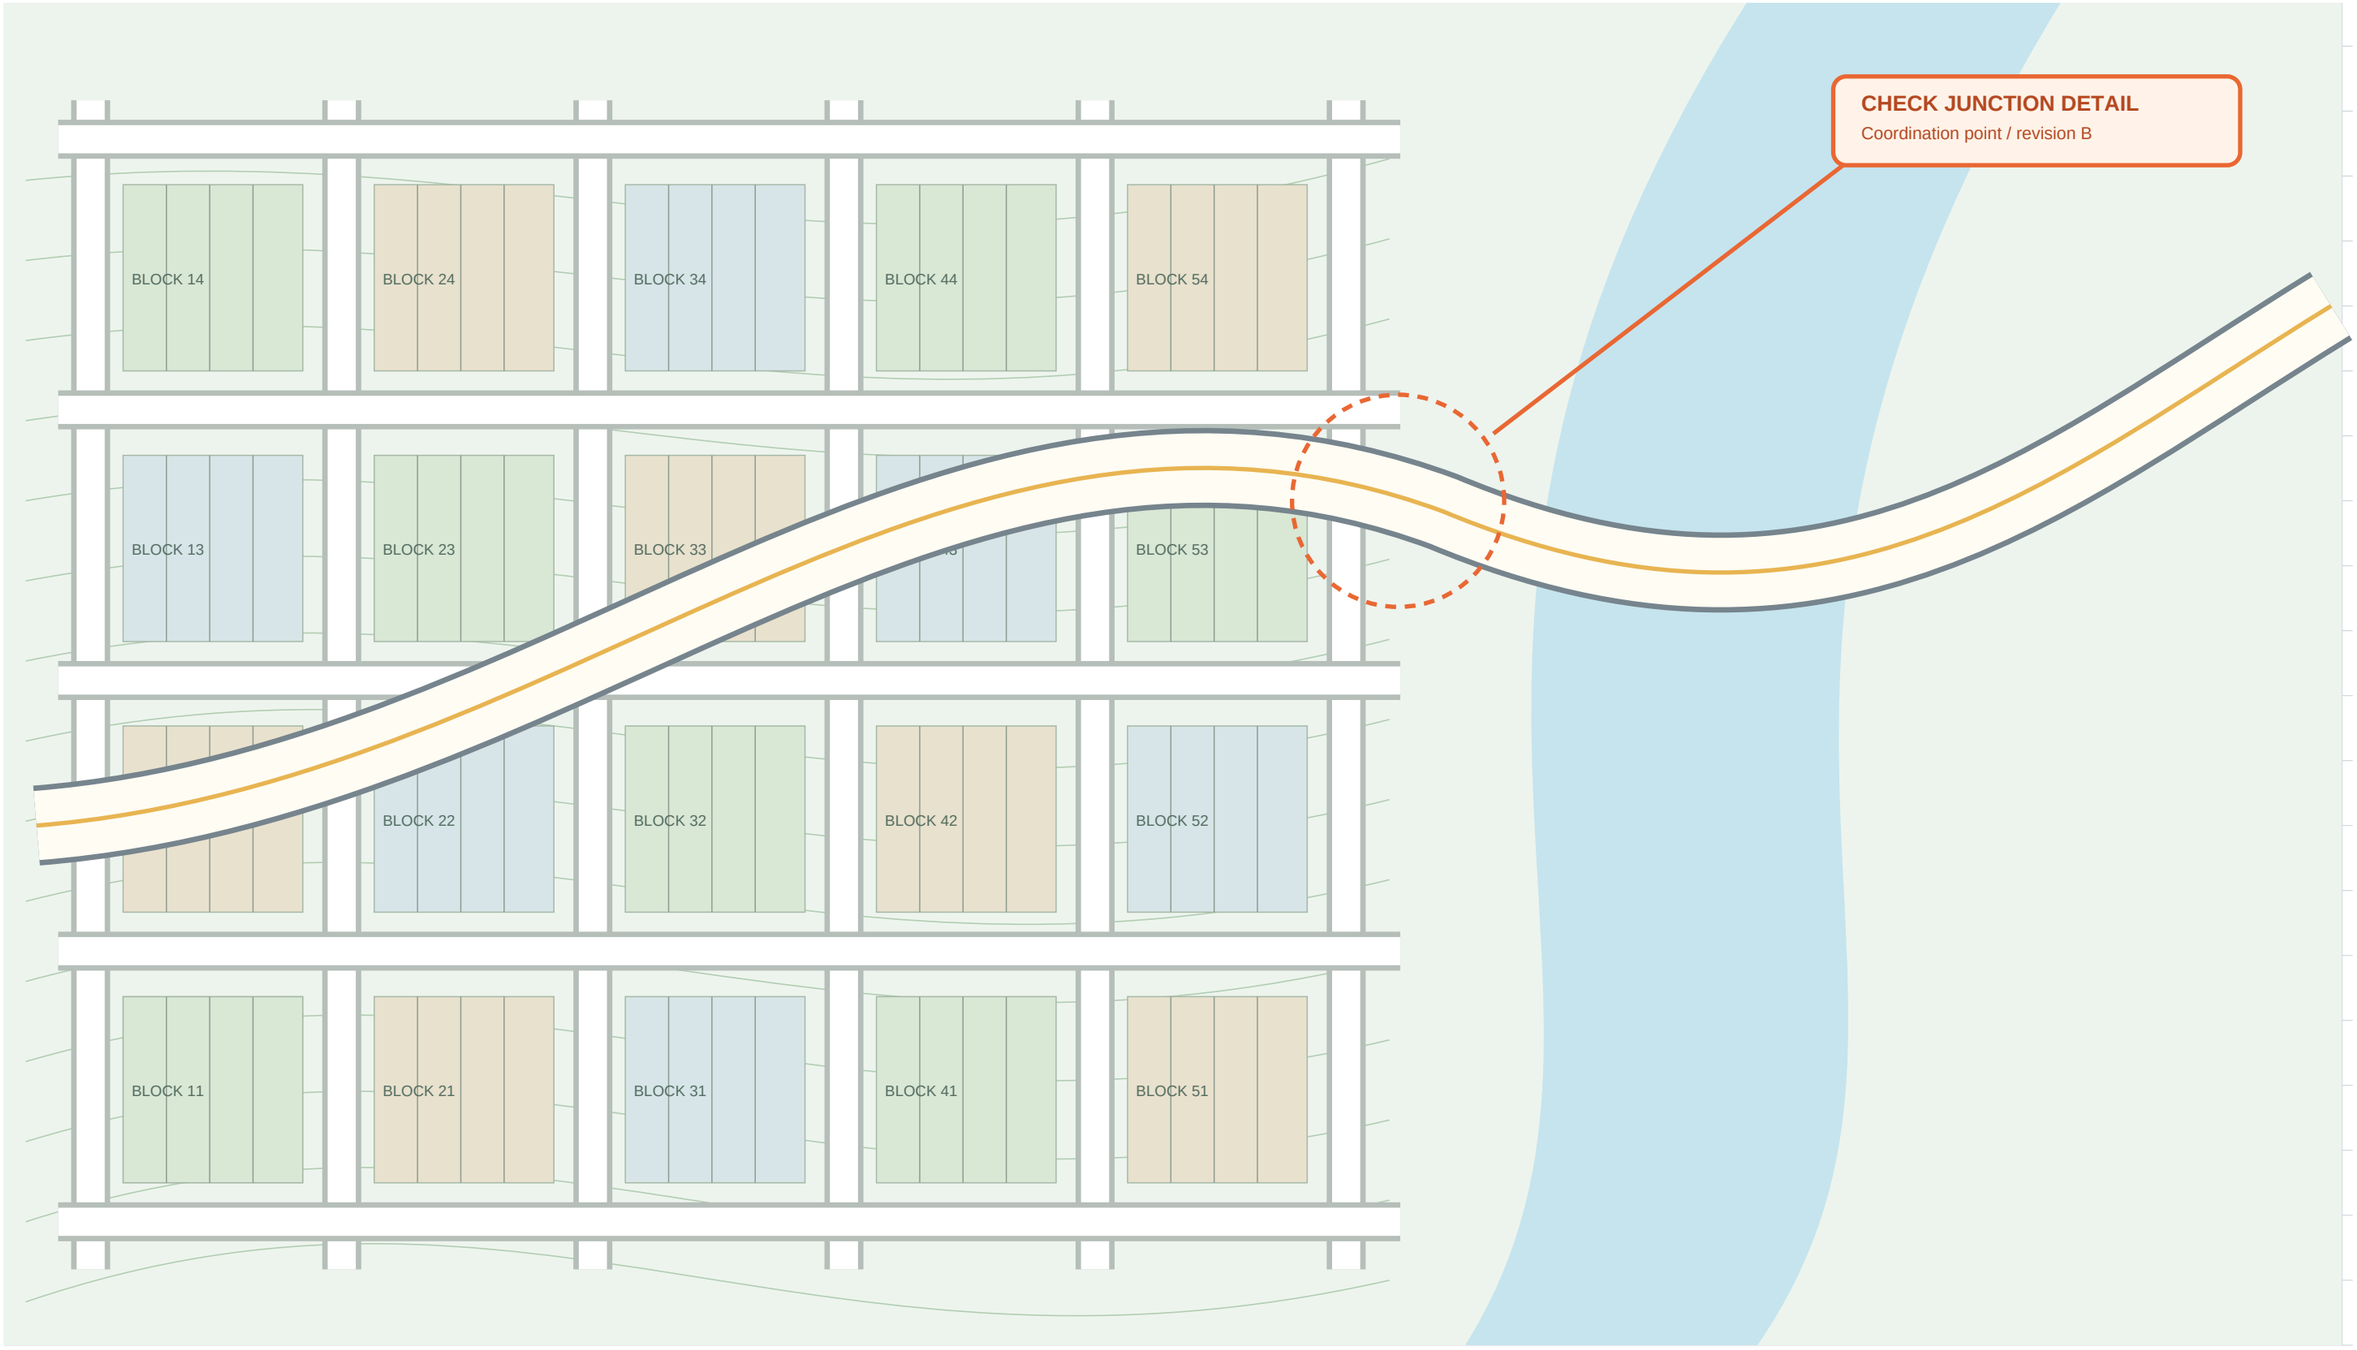

RIVERSIDE / MASTER PLAN

Prepared for PDF Reader Pro product demonstration

SCALE 1:2000

FORMAT A3 / LANDSCAPE

XT-01

SITE COORDINATION PLAN

TECHNICAL DRAWING SET / CONCEPT DESIGN / REVISION B

XT SOLUTION

SAMPLE DOCUMENT - NOT FOR CONSTRUCTION

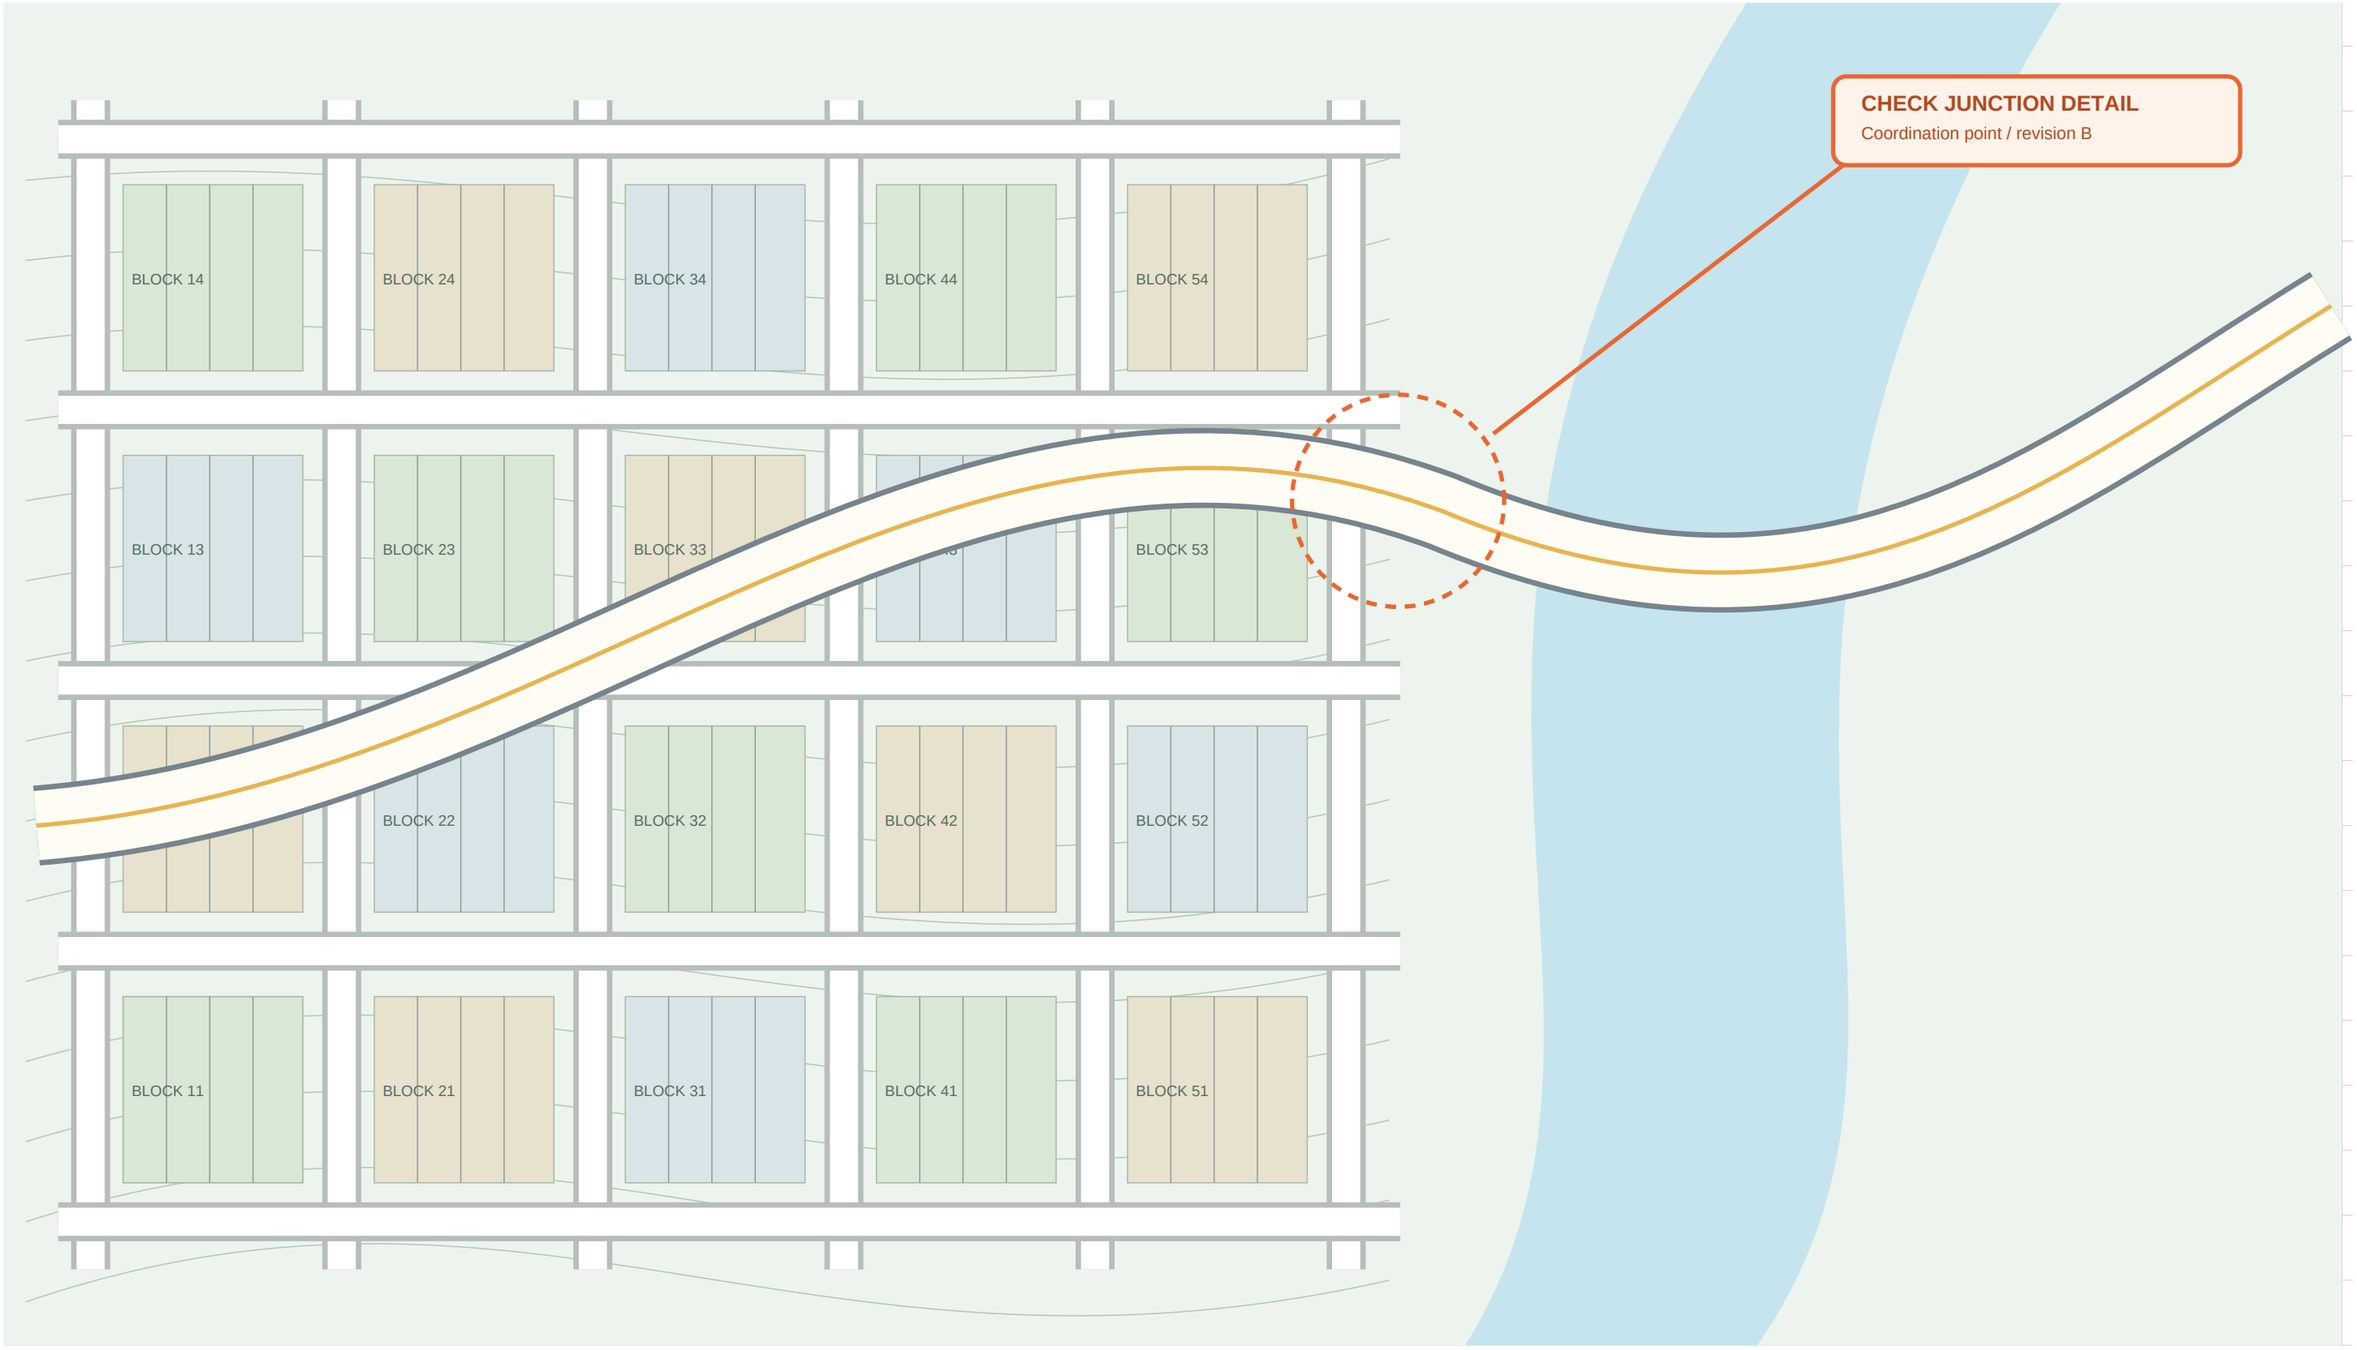

RIVERSIDE / MASTER PLAN

Prepared for PDF Reader Pro product demonstration

SCALE 1:2000

FORMAT A3 / LANDSCAPE

XT-02

LANDSCAPE & ACCESS

TECHNICAL DRAWING SET / CONCEPT DESIGN / REVISION B

XT SOLUTION

SAMPLE DOCUMENT - NOT FOR CONSTRUCTION

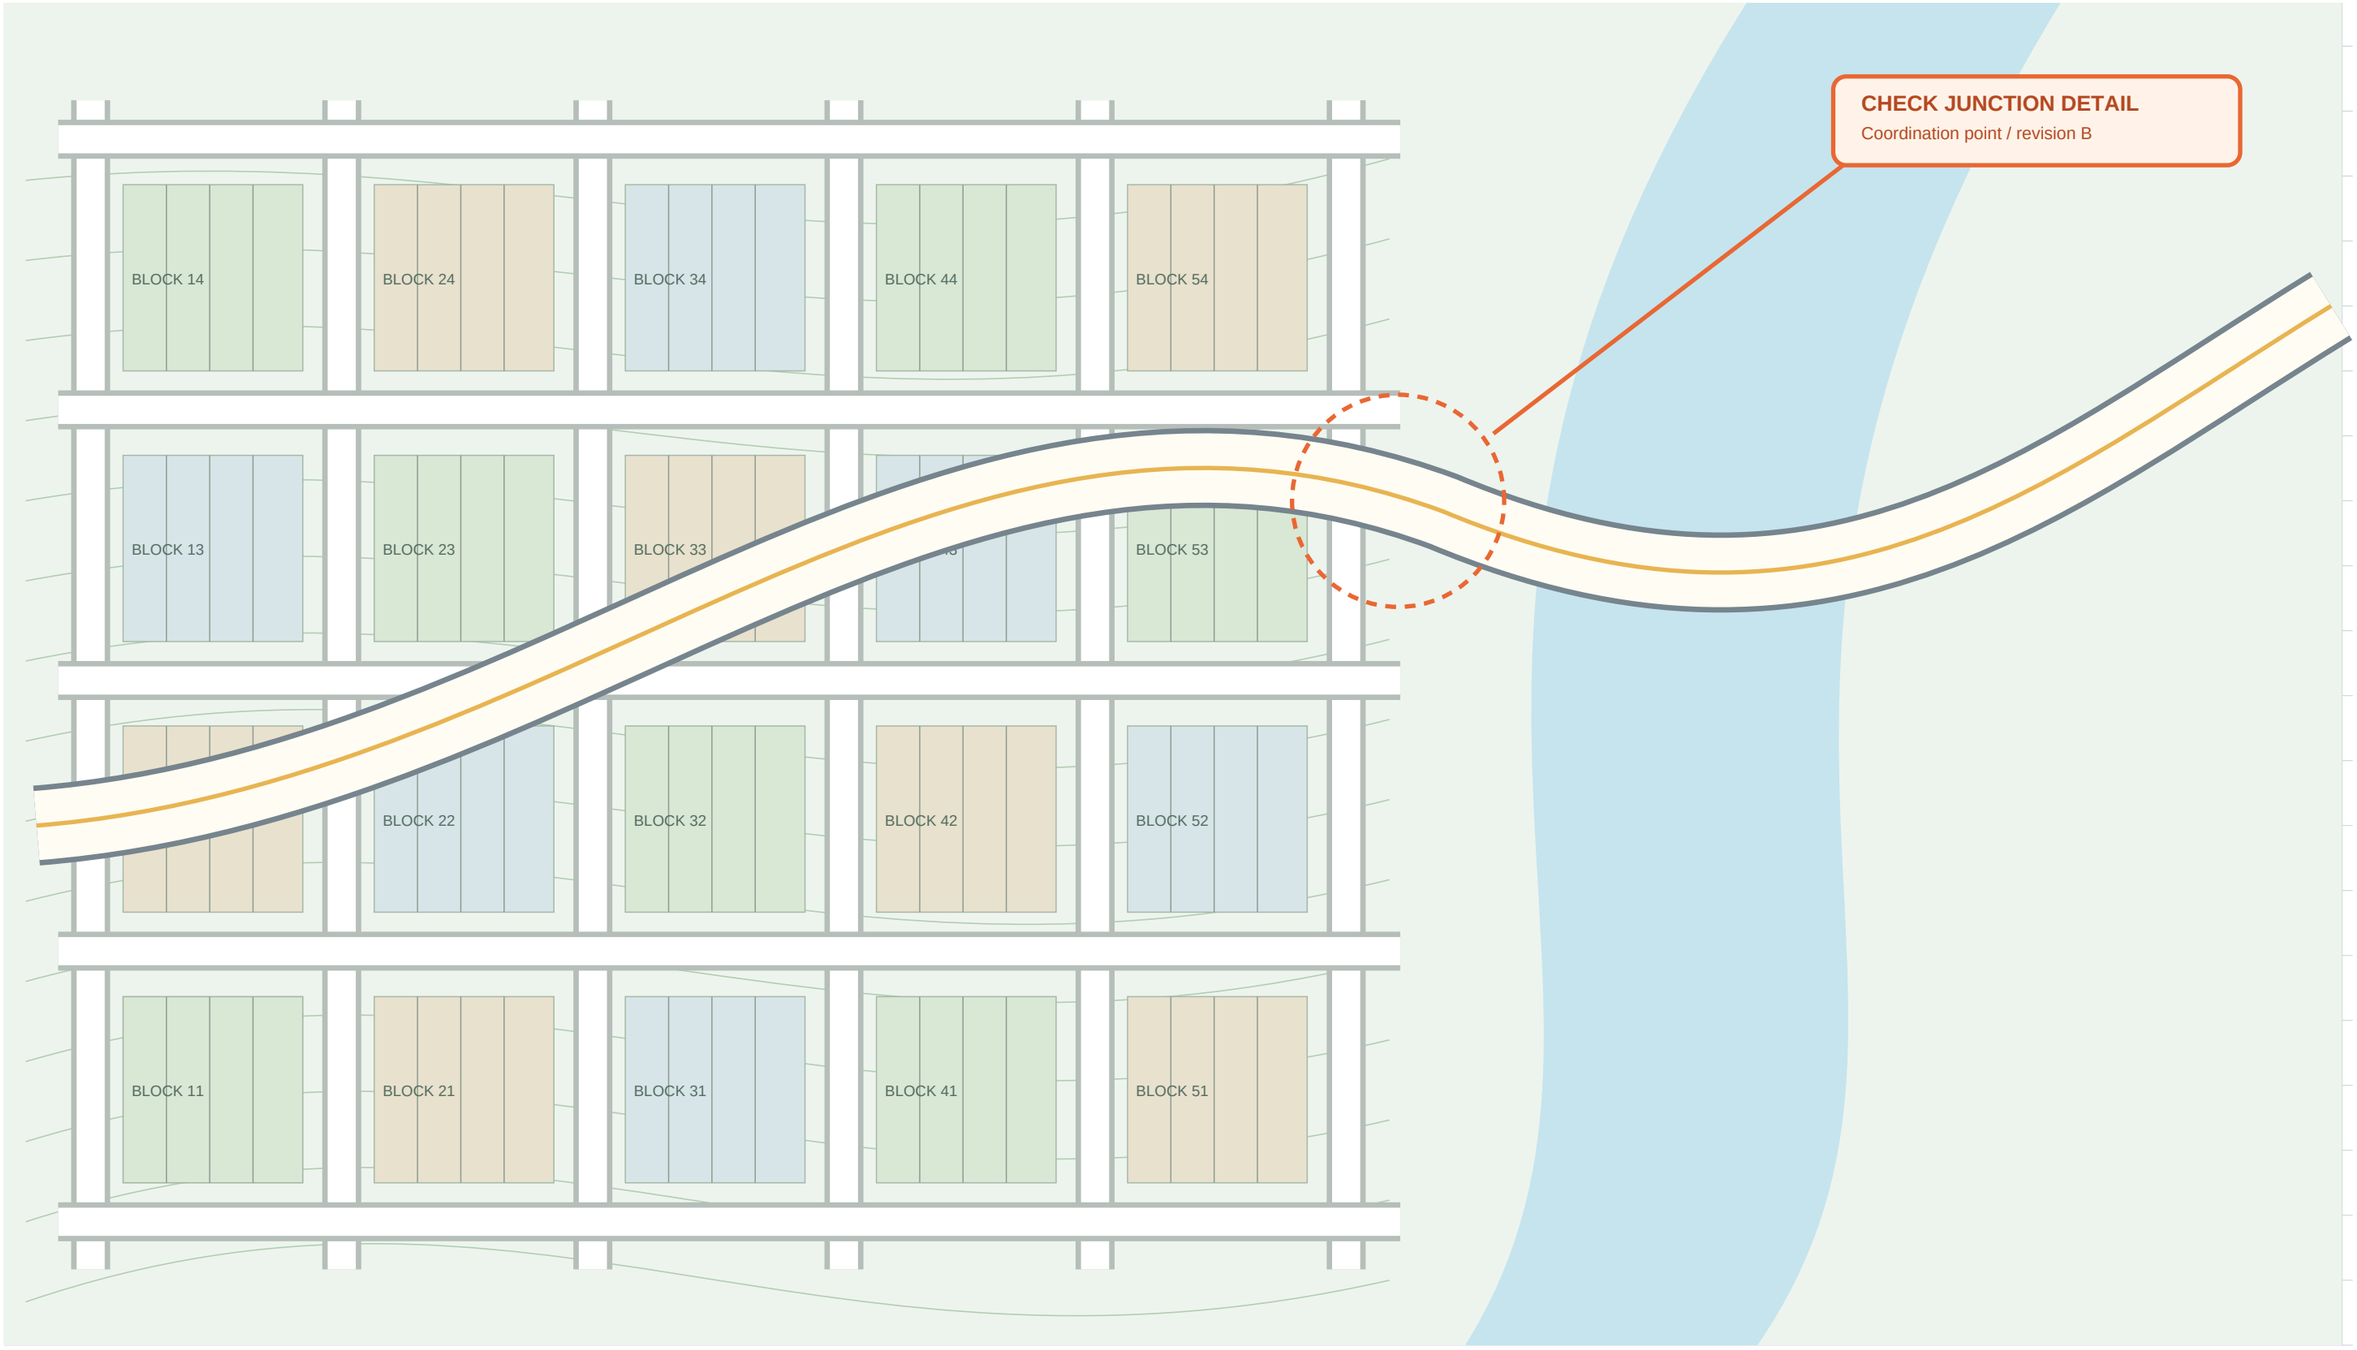

RIVERSIDE / MASTER PLAN

Prepared for PDF Reader Pro product demonstration

SCALE 1:2000

FORMAT A3 / LANDSCAPE

XT-03